


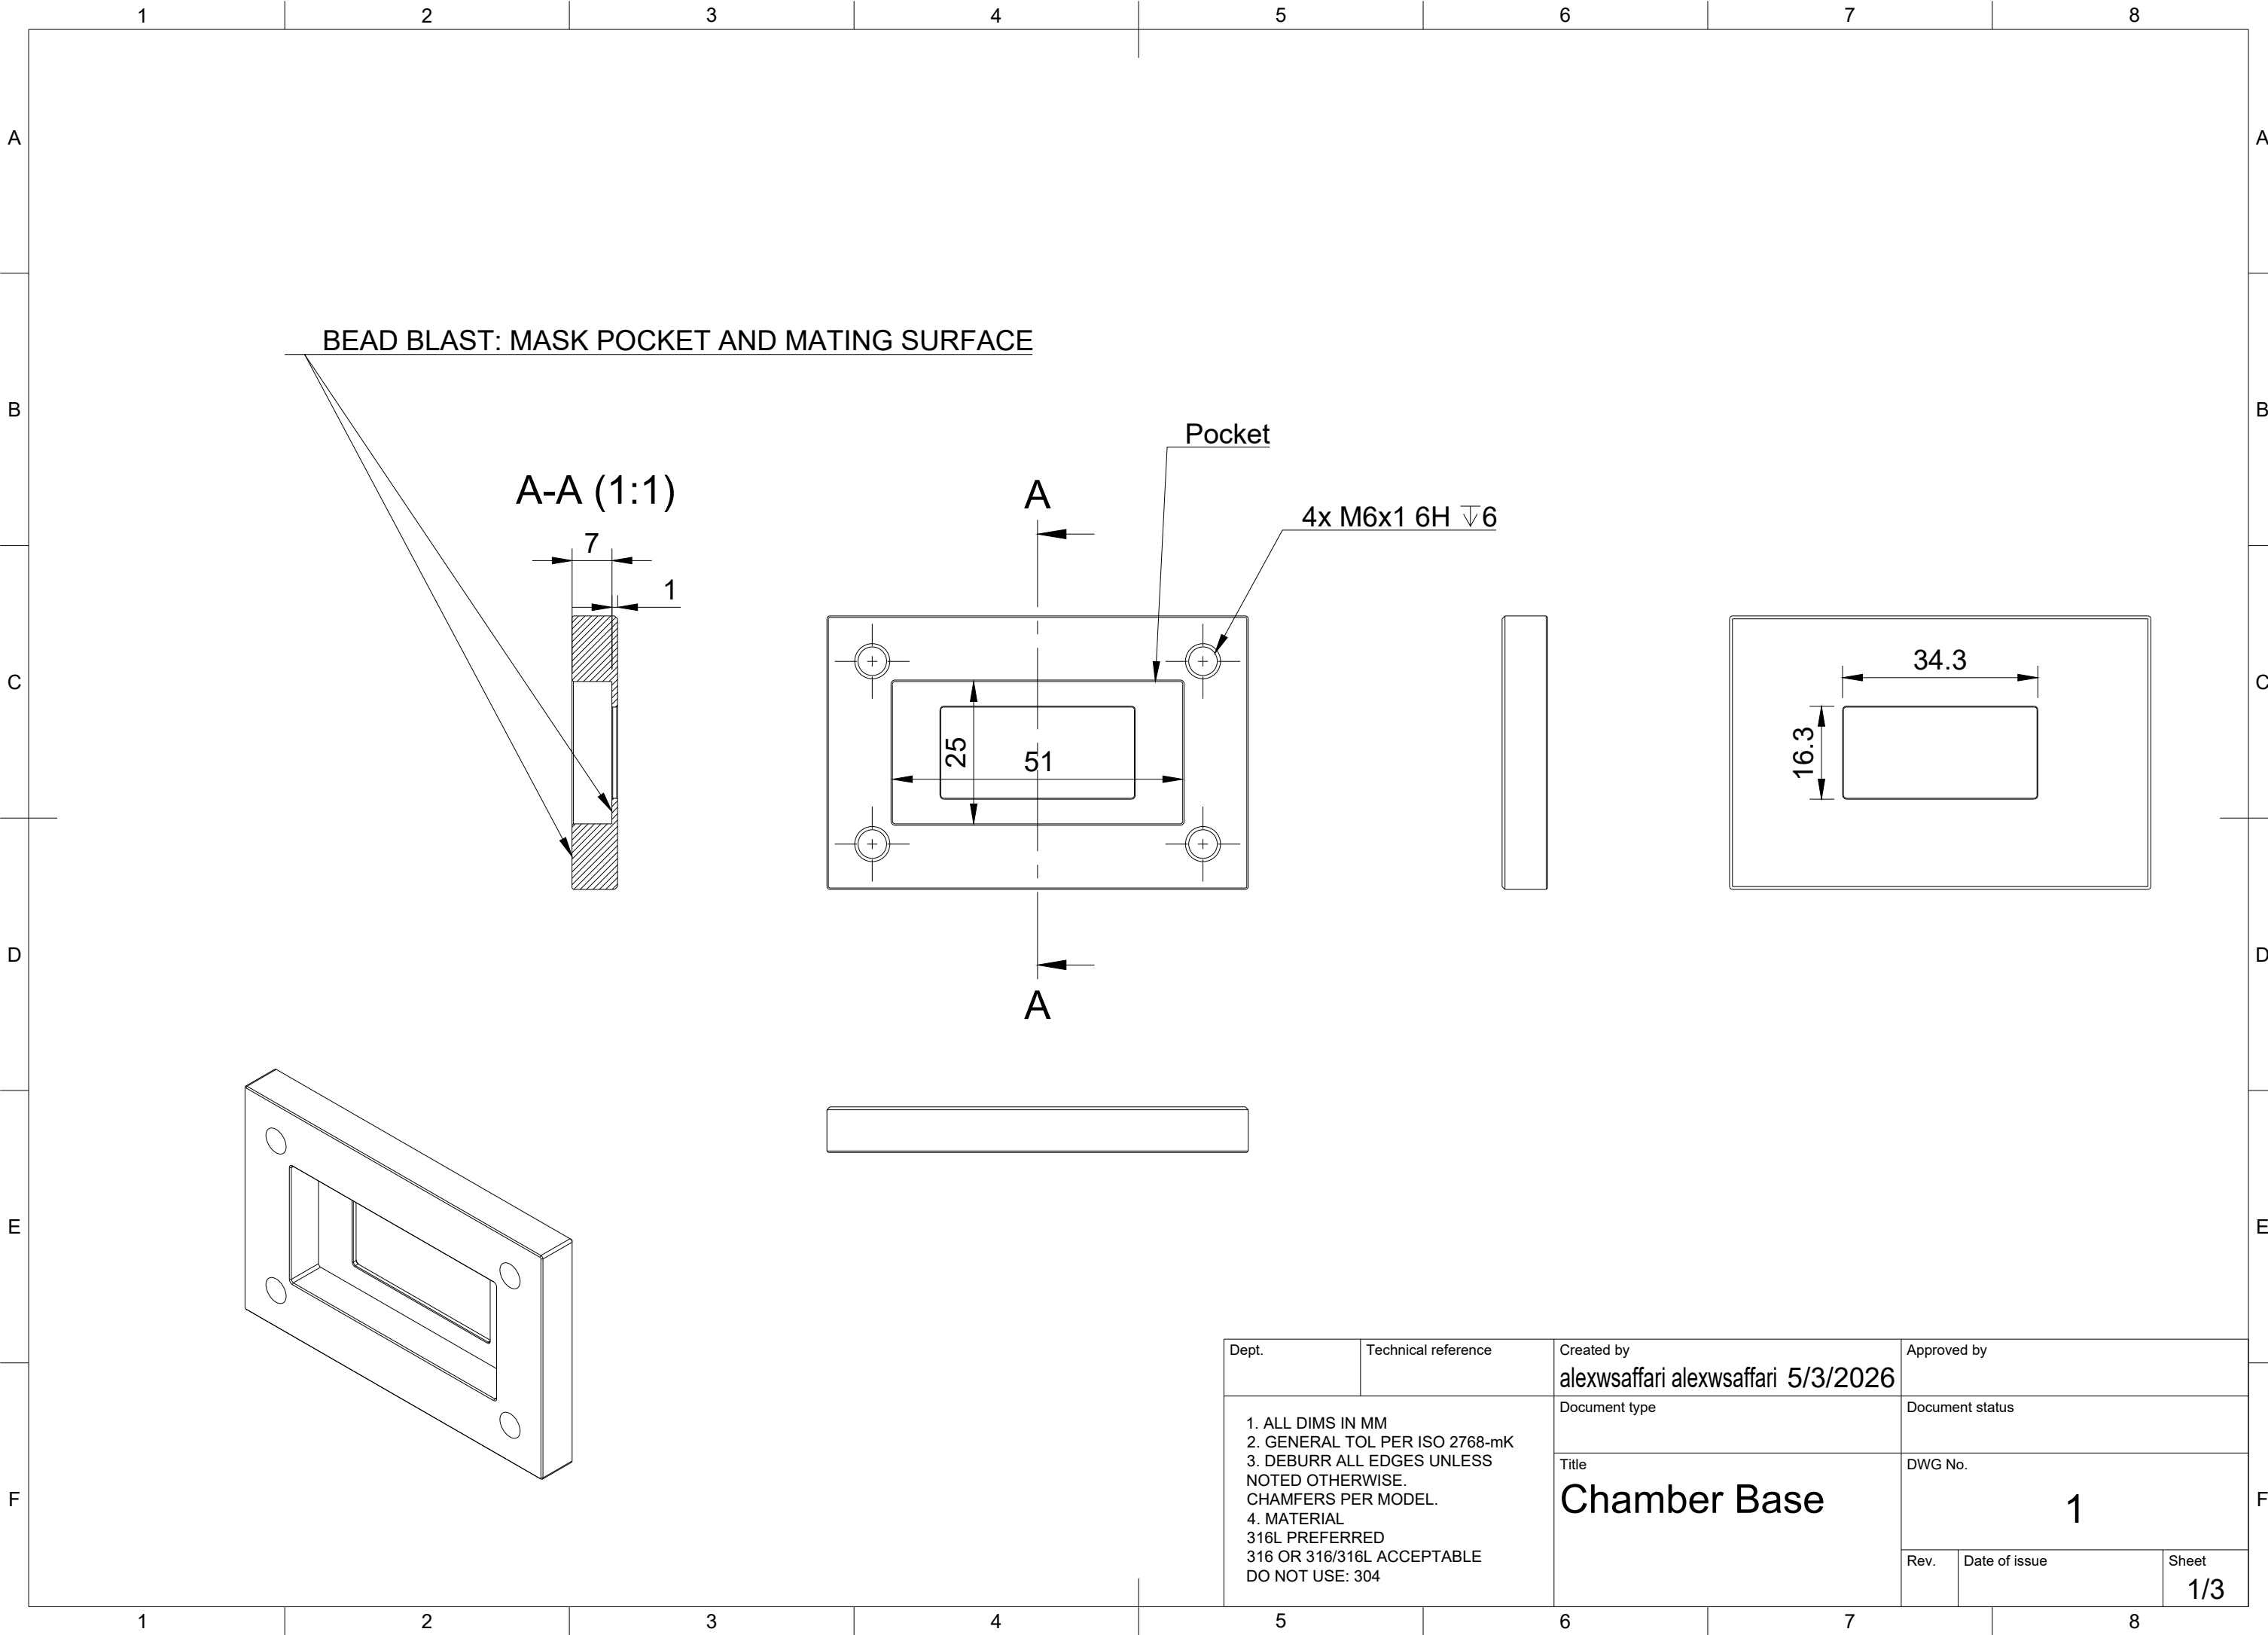

Dept.	Technical reference	Created by alexwsaffari alexwsaffari 5/3/2026	Approved by	
1. ALL DIMS IN MM 2. GENERAL TOL PER ISO 2768-mK 3. DEBURR ALL EDGES UNLESS NOTED OTHERWISE. CHAMFERS PER MODEL. 4. MATERIAL 316L PREFERRED 316 OR 316/316L ACCEPTABLE DO NOT USE: 304		Document type	Document status	
		Title Chamber Base	DWG No. 1	
			Rev.	Date of issue
				Sheet 1/3